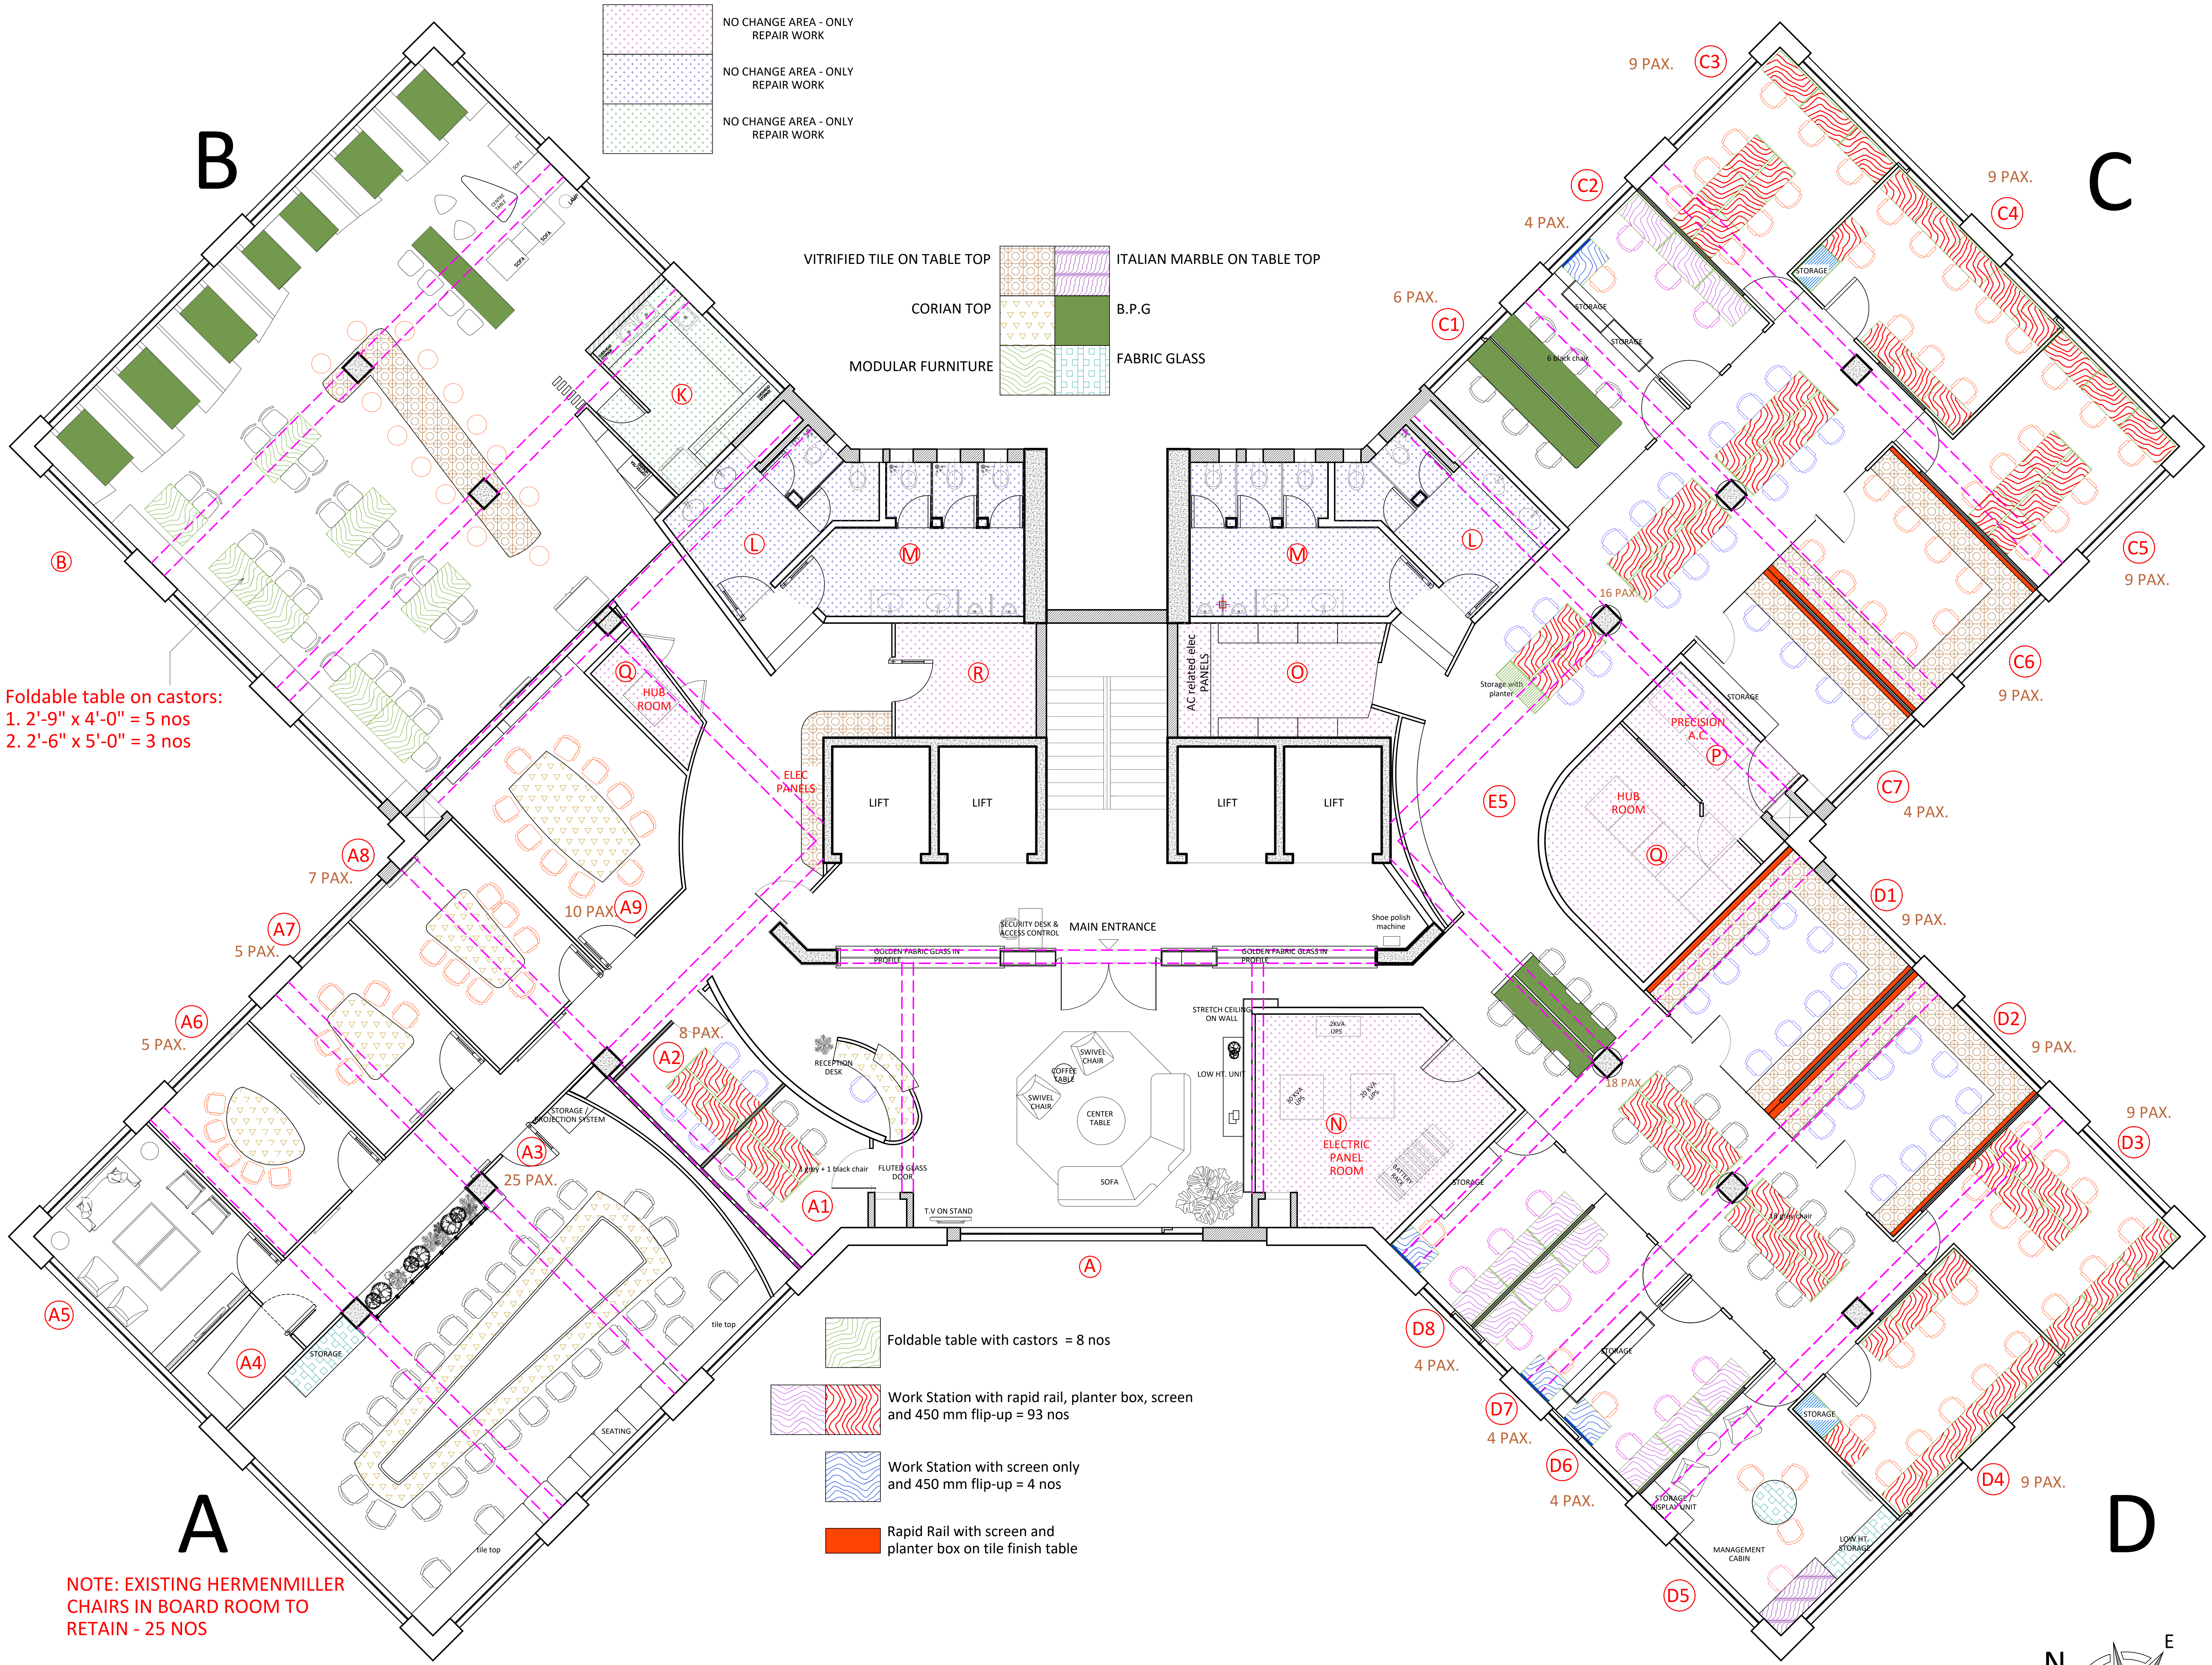

NO CHANGE AREA - ONLY REPAIR WORK
NO CHANGE AREA - ONLY REPAIR WORK
NO CHANGE AREA - ONLY REPAIR WORK

VITRIFIED TILE ON TABLE TOP
ITALIAN MARBLE ON TABLE TOP
CORIAN TOP
B.P.G
MODULAR FURNITURE
FABRIC GLASS

Foldable table on castors:
1. 2'-9" x 4'-0" = 5 nos
2. 2'-6" x 5'-0" = 3 nos

Foldable table with castors = 8 nos

Work Station with rapid rail, planter box, screen and 450 mm flip-up = 93 nos

Work Station with screen only and 450 mm flip-up = 4 nos

🟥 Rapid Rail with screen and planter box on tile finish table

NOTE: EXISTING HERMENMILLER CHAIRS IN BOARD ROOM TO RETAIN - 25 NOS

NOTE: COUNT OTHER CHAIRS THAT ARE RETAINED AT SITE.

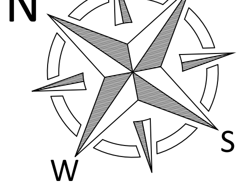

GENERAL NOTES

1. THIS DRAWING IS A RIGHT & PROPERTY OF ELEMENTS. IS NOT TO BE PRODUCED, COPIED, HANDED OVER TO THIRD PARTY OR USED FOR ANY OTHER PURPOSE OTHER THAN FOR WHICH IT IS INTENDED. AND REMAIN OUR SOLE PROPERTY.
2. THIS DRAWING TOGETHER WITH ANY COPIES MADE BY THE RECIPIENT SHALL BE RETURNED ON DEMAND TO US.
3. ONLY WRITTEN DIMENSIONS TO BE FOLLOWED
4. THE PMC/SUPERVISOR/CONTRACTOR/VENDOR MUST CHECK ALL DIMENSIONS AND DETAILS AND BE RESPONSIBLE FOR THE SAME ANY DISCREPANCY SHALL BE BROUGHT TO THE NOTICE OF THE INTERIOR DESIGNER.
5. THIS DRAWING SHOULD BE READ IN CONJUNCTION WITH RELEVANT WORKING AND DETAIL DRAWINGS
6. ALL DIMENSIONS SHALL BE VERIFIED ON SITE PRIOR TO COMMENCEMENT OF WORK
7. ALL DIMENSIONS ARE IN INCHES UNLESS OTHERWISE MENTIONED
8. ALL LEVELS INDICATED ARE IN FEET UNLESS OTHERWISE MENTIONED
9. DIMENSIONS/LEVELS INDICATED ARE STRUCTURAL UNLESS OTHERWISE MENTIONED
10. THIS DRAWING, UNLESS OTHERWISE MENTIONED, TO BE PLOTTED MENTIONED PAPER SIZE
11. RELEVANT SERVICES DRAWINGS ARE TO READ SIMULTANEOUSLY AND PROVISION OF CUTOUT SLEEVES PROVIDED AS REQUIRED
12. ALL MATERIALS/FINISHES TO BE AS SPECIFIED AND APPROVED BY THE INTERIOR DESIGNER

REVISIONS

REV NO. (n)	DATE	DESCRIPTION
1.	DD-MM-YYYY	DESCRIPTION
2.		
3.		
4.		
5.		
6.		
7.		
8.		
9.		
10.		
11.		
12.		
13.		
14.		
15.		
16.		
17.		
18.		
19.		
20.		

DRAWING TITLE

FURNITURE LAYOUT

DWG ISSUED FOR

☑ ADVANCE COPY
☑ APPROVAL
☐ TENDER
☑ COMMENTS
☐ EXECUTION
☐ RECORD
☐ CONTRACTOR
☐ PMC

SCHEDULE OF AREA

AREA OF LIFT LOBBY		299
AREA OF PREMISES WITH COLUMNS & DUCTS		11270
	PREMISES (SQ.FT.)	TERR. AREA (SQ.FT.)
TOTAL AREA	10,414	

CLIENT REQUIREMENTS

STAMP AND SIGN

1. A1 =	4 PAX
2. A2 =	4 PAX
3. D1 =	9 PAX
4. D2 =	9 PAX
5. D3 =	9 PAX
6. D4 =	9 PAX
7. D5 =	1 PAX
8. D6 =	4 PAX
9. D7 =	4 PAX
10. D8 =	4 PAX
11. PASSAGE =	18 PAX
11. C1 =	6 PAX
12. C2 =	4 PAX
13. C3 =	9 PAX
14. C4 =	9 PAX
15. C5 =	9 PAX
16. C6 =	9 PAX
17. C7 =	4 PAX
18. PASSAGE =	16 PAX
TOTAL WORKING PEOPLE =	141 PAX

NOTE: CONFERENCE AREA AND CAFETERIA NOT INCLUDED.

1. PARTNER =	16 PAX
2. ARTICLE =	62 PAX
3. C.A =	54 PAX
4. ADMIN/HR/ I.T =	8 PAX
5. Management cabin =	1 pax
	141 PAX

NEETAARA
INTERIOR DESIGNERS, CONSULTANTS & STYLISTS
5th Flr, ITTS House, Kala ghoda, Mumbai,
Maharashtra 400001
E: shitaldjhaveri@gmail.com
M: +91 9322230804

CLIENT
CBVA

PROJECT LOCATION: NARIMAN BHAVAN, NARIMAN POINT - MUMBAI

PURPOSE OF RELEASE
MODULAR AND FIX FURNITURE

START DATE	19-03-2025	ISSUE DATE	12-06-2025
DRAWN BY	TA	CHECKED BY	SDJ

DIRECTION

DRAWING NO.
009

REVISION NO.
R007

THIS IS THE SOLE PROPERTY OF NEETARA. IT'S USE FOR ANY OTHER PURPOSE OTHER THAN THAT MENTIONED IS TO BE DONE ONLY AFTER PRIOR APPROVAL